
TS 11/14/18 · Ward-16 Thallakulam · Madurai North

MASSING — 20 ft slanted road, one rectangle, three triangles

scale 1:250 — print at 100% on A3

north up · all figures in feet

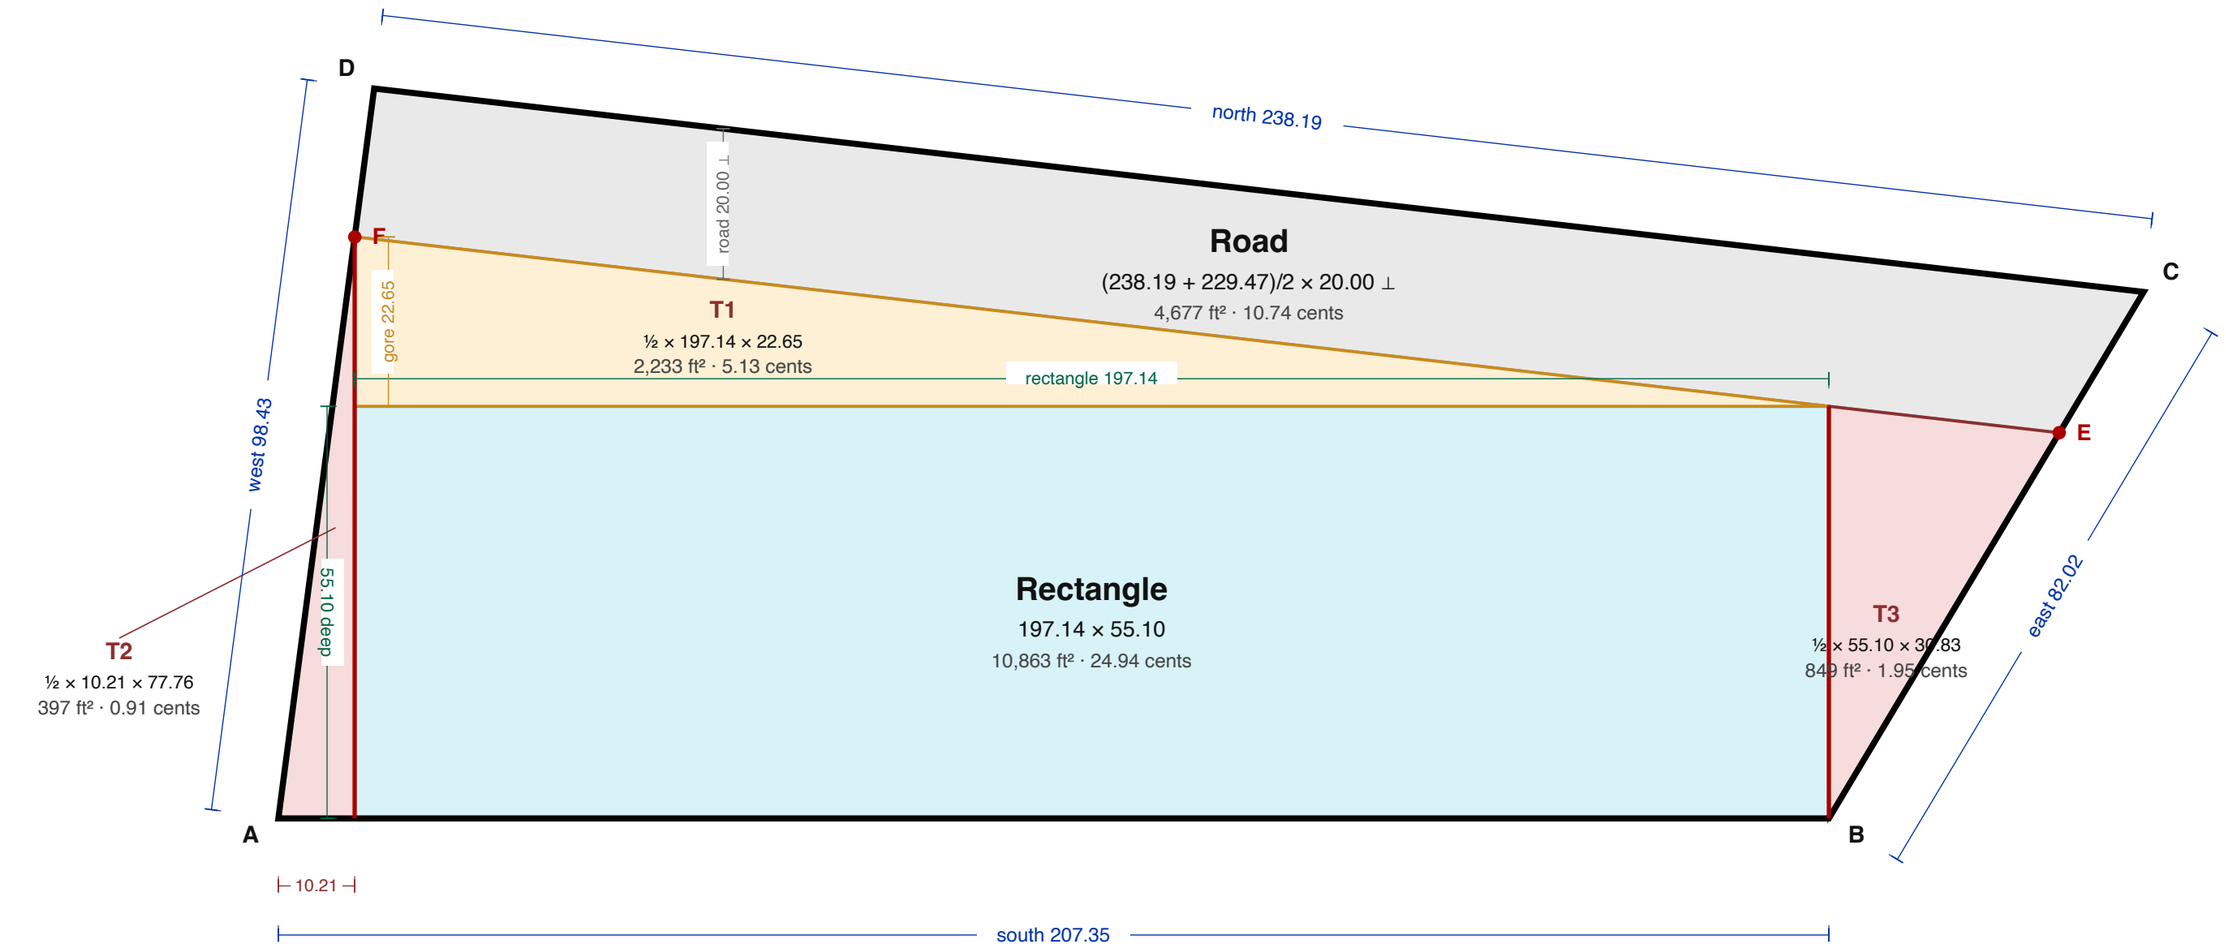

SCHEDULE — 20 ft road, north boundary slants 6.56°

piece	sides (ft)	area = base × height	area ft²	cents	m²
Road	229.47 × 21.95 × 238.19 × 20.00	(238.19 + 229.47)/2 × 20.00 ⊥	4,677	10.74	434.5
Rectangle	**197.14 × 55.10 × 197.14 × 55.10**	**197.14 × 55.10**	**10,863**	**24.94**	**1009.2**
T1 gore	197.14 × 198.44 × 22.65	½ × 197.14 × 22.65	2,233	5.13	207.5
T2 west corner	10.21 × 77.76 × 78.42	½ × 10.21 × 77.76	397	0.91	36.9
T3 east corner	60.07 × 31.03 × 55.10	½ × 55.10 × 30.83	849	1.95	78.9
TOTAL			**19,019**	**43.66**	**1766.9**

TALLY road 4,677 + rectangle 10,863 + triangles 3,479 = 19,019 ft² = 43.66 cents = 1766.9 m² = the whole plot

SCALE 1:250 — 1 mm on paper = 0.25 m = 0.82 ft on the ground

0 5 10 15 20 25 m


this bar is exactly 100 mm — check it with a ruler; if it differs the print was resized

TS 11/14/18 · Ward-16 Thallakulam · Madurai North

MASSING — 15 ft slanted road, one rectangle, three triangles

scale 1:250 — print at 100% on A3

north up · all figures in feet

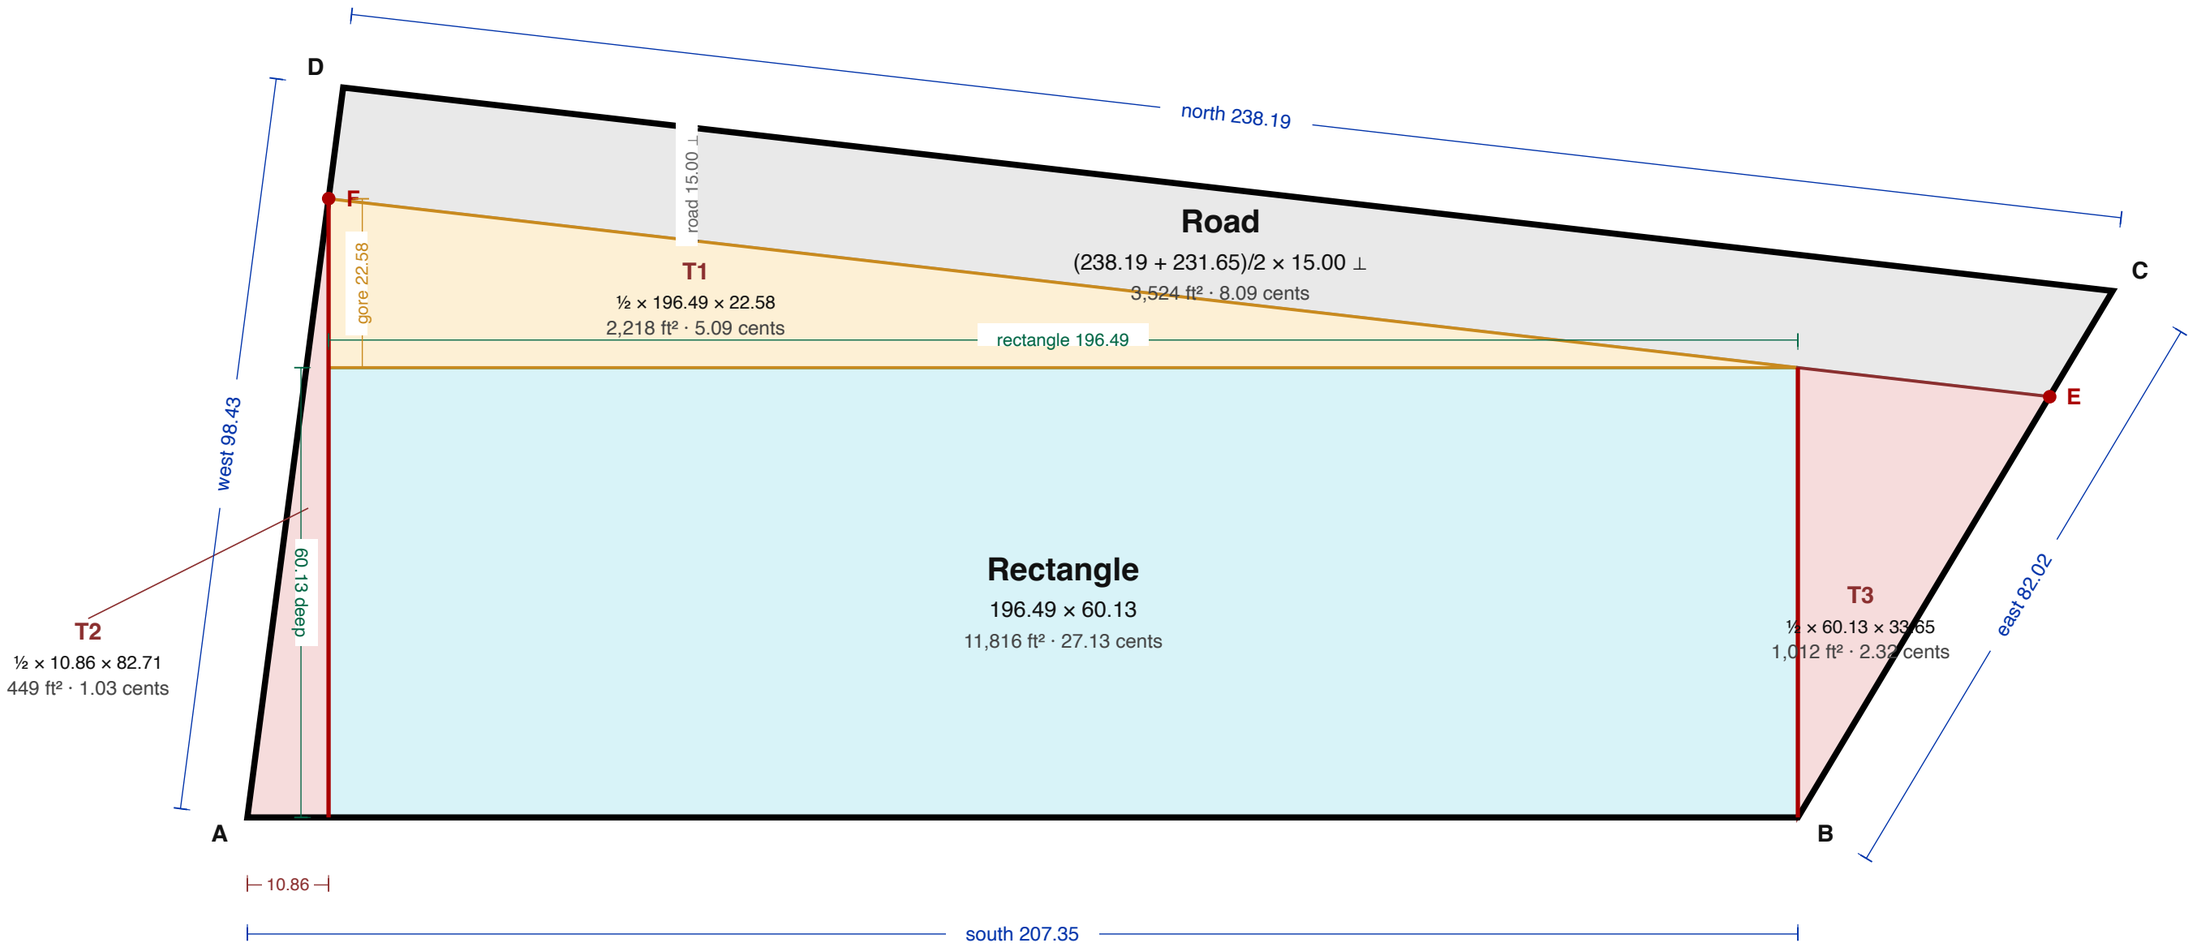

SCHEDULE — 15 ft road, north boundary slants 6.56°

piece	sides (ft)	area = base × height	area ft²	cents	m²
Road	231.65 × 16.46 × 238.19 × 15.00	(238.19 + 231.65)/2 × 15.00 ⊥	3,524	8.09	327.4
Rectangle	**196.49 × 60.13 × 196.49 × 60.13**	**196.49 × 60.13**	**11,816**	**27.13**	**1097.7**
T1 gore	196.49 × 197.78 × 22.58	½ × 196.49 × 22.58	2,218	5.09	206.1
T2 west corner	10.86 × 82.71 × 83.42	½ × 10.86 × 82.71	449	1.03	41.7
T3 east corner	65.56 × 33.87 × 60.13	½ × 60.13 × 33.65	1,012	2.32	94.0
TOTAL			**19,019**	**43.66**	**1766.9**

TALLY road 3,524 + rectangle 11,816 + triangles 3,679 = 19,019 ft² = 43.66 cents = 1766.9 m² = the whole plot

SCALE 1:250 — 1 mm on paper = 0.25 m = 0.82 ft on the ground

0 5 10 15 20 25 m

this bar is exactly 100 mm — check it with a ruler; if it differs the print was resized